


Поз. обозначение	Наименование	Кол-во
M1	Электродвигатель	1
TC	Понижающий трансформатор	1
V1, V2	Диодный мост (выпрямитель)	2
KM1...3	Контактор	3
QF1, QF2	Автоматический выключатель	2
KK1	Тепловое реле	1
KT1	Реле времени	1
SB1	Кнопка «Стоп»	1
SB2	Кнопка «Пуск»	1
SB3	Кнопка «Назад»	1
HL1...3	Лампа сигнальная	3
HL2	Лампа сигнальная	1
HL3	Лампа сигнальная	1

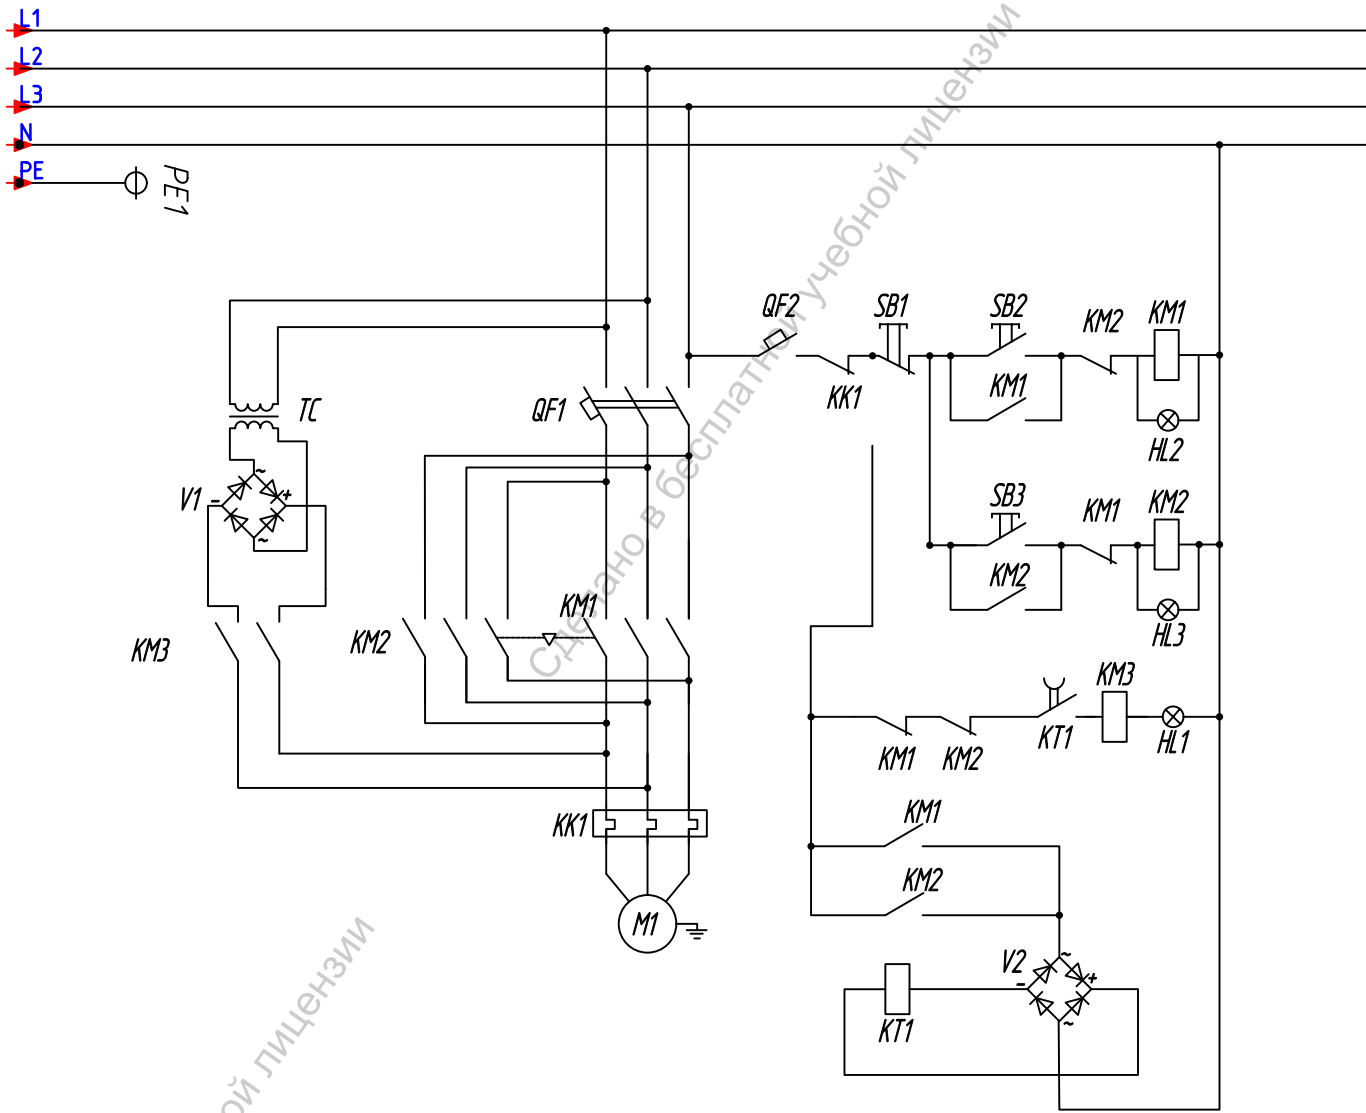

Согласовано

Взам. инв. №

Подп. и дата

Инв. № подл.

Изм.	Кол. уч.	Лист	№ док.	Подп.	Дата

Стадия	Лист	Листов